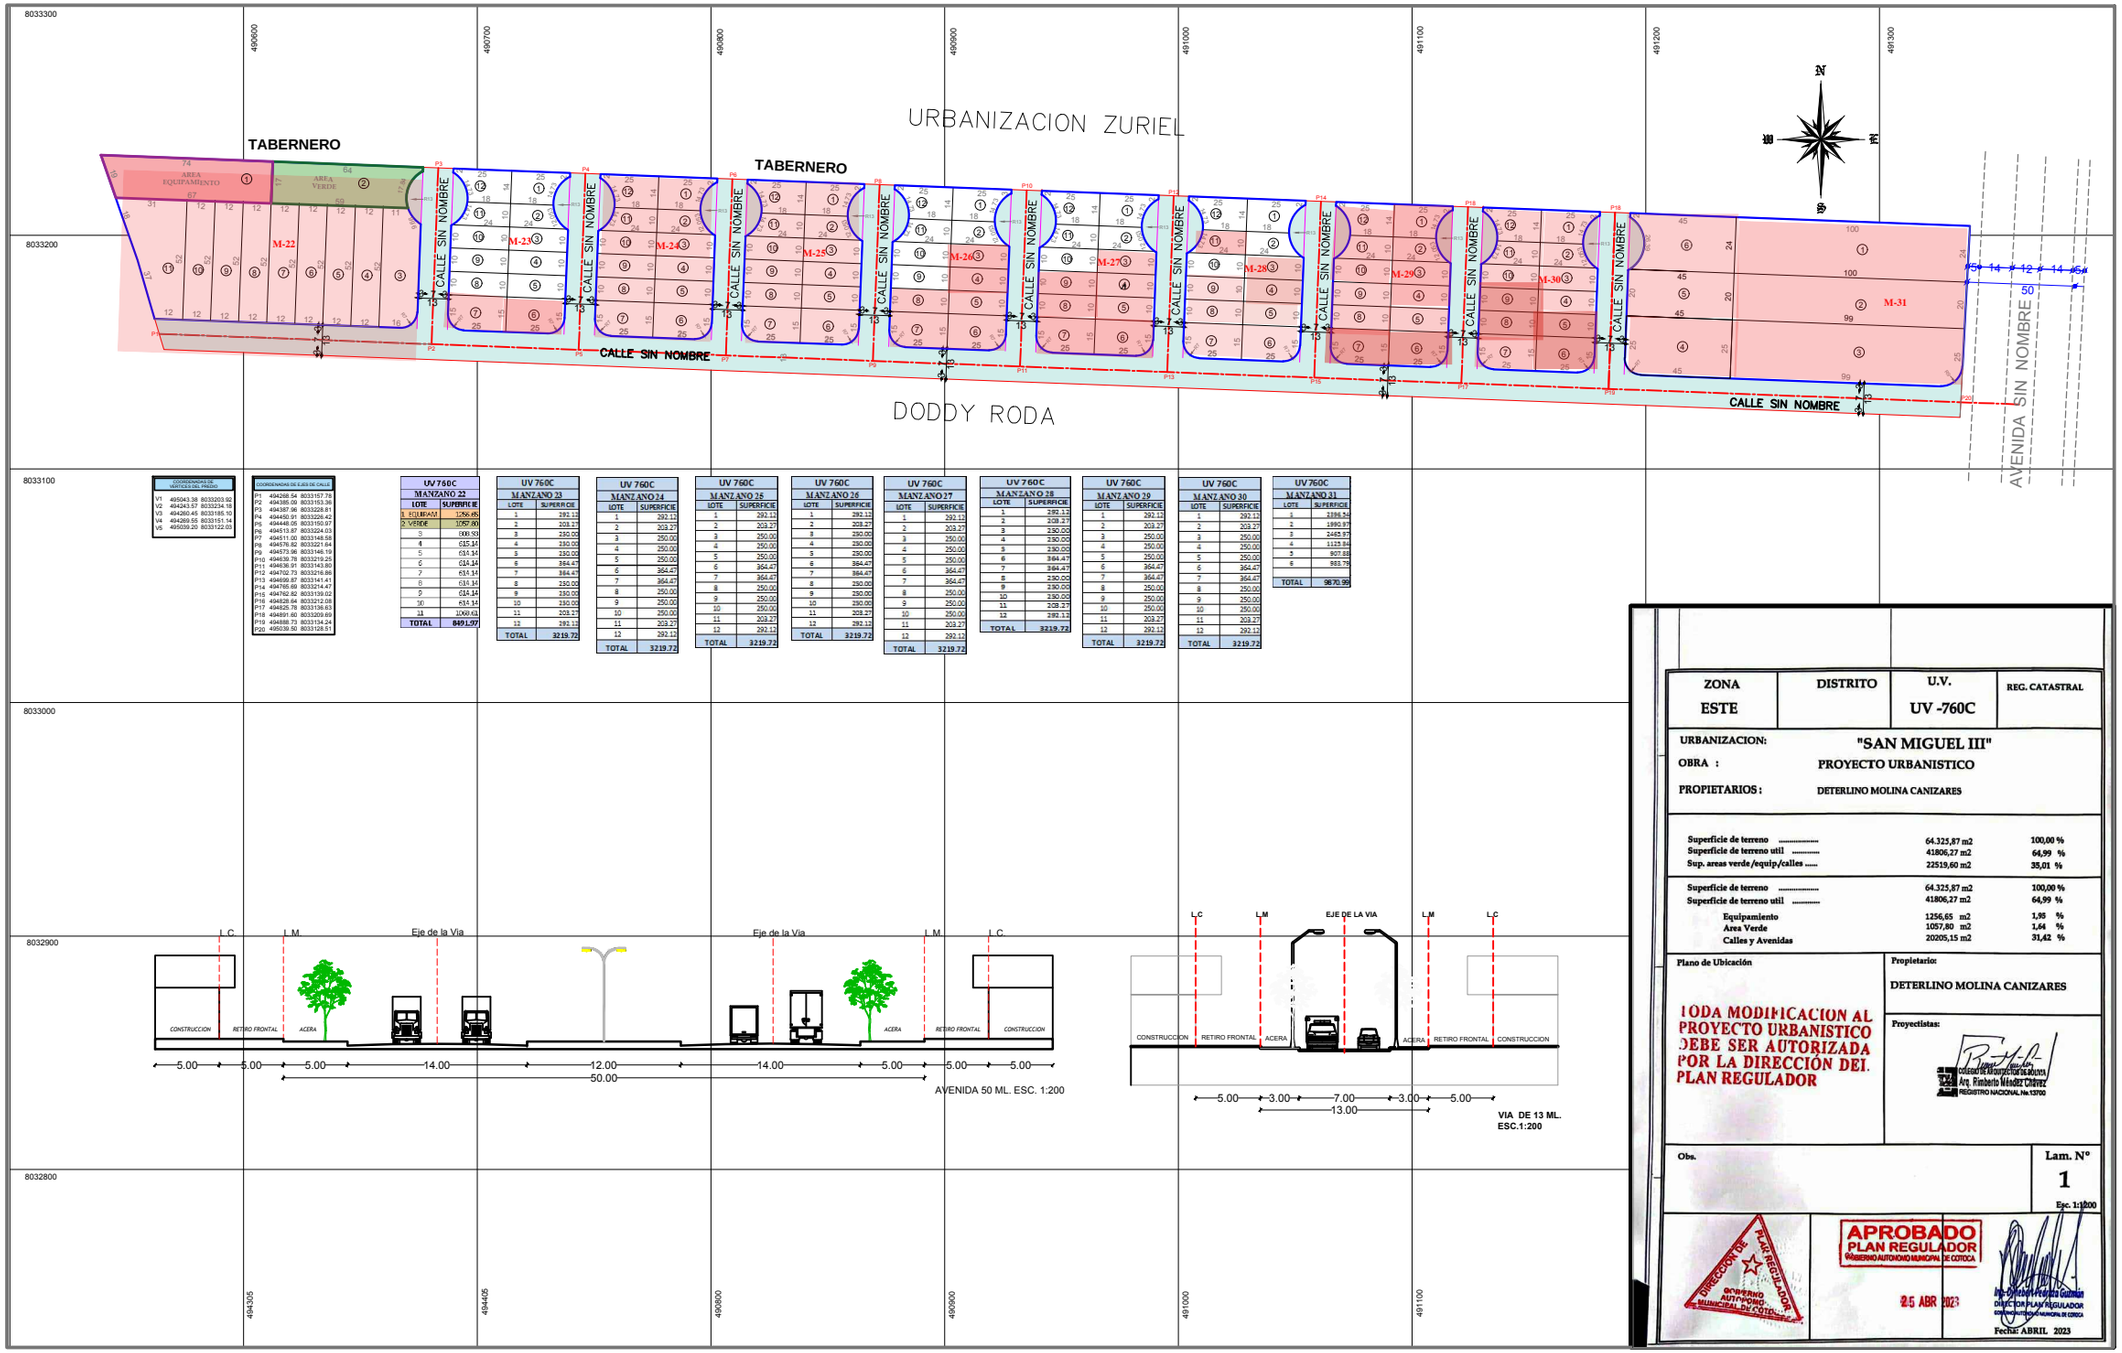

COORDENADAS DE MONTEALTO DEL PREDIO		
V1	495043.38	8033203.92
V2	494243.57	8033234.18
V3	494240.45	8033185.10
V4	494269.55	8033151.14
V5	495039.20	8033122.03

COORDENADAS DE EJES DE CALLE		
P1	494268.54	8033157.76
P2	494385.08	8033153.36
P3	494387.96	8033228.81
P4	494450.91	8033226.42
P5	494448.05	8033150.97
P6	494513.87	8033224.03
P7	494511.00	8033148.58
P8	494576.82	8033221.64
P9	494573.96	8033146.19
P10	494639.78	8033219.25
P11	494636.91	8033143.80
P12	494702.73	8033216.86
P13	494699.87	8033141.41
P14	494765.68	8033214.47
P15	494762.82	8033139.02
P16	494828.64	8033212.08
P17	494825.78	8033136.63
P18	494891.60	8033209.69
P19	494888.73	8033134.24
P20	495039.50	8033128.51

UV 760C MANZANO 22	
LOTE	SUPERFICIE
1 EQUIPAMIENTO	1256,65
2 VERDE	1057,80
3	890,93
4	635,14
5	635,14
6	635,14
7	635,14
8	635,14
9	635,14
10	635,14
11	1049,63
TOTAL	8491,97

UV 760C MANZANO 23	
LOTE	SUPERFICIE
1	292,12
2	203,27
3	250,00
4	250,00
5	250,00
6	364,47
7	364,47
8	250,00
9	250,00
10	250,00
11	203,27
12	292,12
TOTAL	3219,72

UV 760C MANZANO 24	
LOTE	SUPERFICIE
1	292,12
2	203,27
3	250,00
4	250,00
5	250,00
6	364,47
7	364,47
8	250,00
9	250,00
10	250,00
11	203,27
12	292,12
TOTAL	3219,72

UV 760C MANZANO 25	
LOTE	SUPERFICIE
1	292,12
2	203,27
3	250,00
4	250,00
5	250,00
6	364,47
7	364,47
8	250,00
9	250,00
10	250,00
11	203,27
12	292,12
TOTAL	3219,72

UV 760C MANZANO 26	
LOTE	SUPERFICIE
1	292,12
2	203,27
3	250,00
4	250,00
5	250,00
6	364,47
7	364,47
8	250,00
9	250,00
10	250,00
11	203,27
12	292,12
TOTAL	3219,72

UV 760C MANZANO 27	
LOTE	SUPERFICIE
1	292,12
2	203,27
3	250,00
4	250,00
5	250,00
6	364,47
7	364,47
8	250,00
9	250,00
10	250,00
11	203,27
12	292,12
TOTAL	3219,72

UV 760C MANZANO 28	
LOTE	SUPERFICIE
1	292,12
2	203,27
3	250,00
4	250,00
5	250,00
6	364,47
7	364,47
8	250,00
9	250,00
10	250,00
11	203,27
12	292,12
TOTAL	3219,72

UV 760C MANZANO 29	
LOTE	SUPERFICIE
1	292,12
2	203,27
3	250,00
4	250,00
5	250,00
6	364,47
7	364,47
8	250,00
9	250,00
10	250,00
11	203,27
12	292,12
TOTAL	3219,72

UV 760C MANZANO 30	
LOTE	SUPERFICIE
1	292,12
2	203,27
3	250,00
4	250,00
5	250,00
6	364,47
7	364,47
8	250,00
9	250,00
10	250,00
11	203,27
12	292,12
TOTAL	3219,72

UV 760C MANZANO 31	
LOTE	SUPERFICIE
1	2386,54
2	1990,97
3	2485,97
4	1125,84
5	907,88
6	983,79
TOTAL	9870,99

AVENIDA 50 ML. ESC. 1:200

VIA DE 13 ML.
ESC.1:200

ZONA	DISTRITO	U.V.	REG. CATASTRAL
ESTE		UV -760C	

URBANIZACION: "SAN MIGUEL III"

OBRA : PROYECTO URBANISTICO

PROPIETARIOS : DETERLINO MOLINA CANIZARES

Superficie de terreno	64.325,87 m2	100,00 %
Superficie de terreno util	41806,27 m2	64,99 %
Sup. areas verde /equip/calles	22519,60 m2	35,01 %

Superficie de terreno	64.325,87 m2	100,00 %
Superficie de terreno util	41806,27 m2	64,99 %
Equipamiento	1256,65 m2	1,95 %
Area Verde	1057,80 m2	1,64 %
Calles y Avenidas	20205,15 m2	31,42 %

Plano de Ubicación

Propietario:
DETERLINO MOLINA CANIZARES

Proyectistas:
Arq. Rimberto Méndez Chávez
COLEGIO DE ARQUITECTOS DE BOLIVIA
REGISTRO NACIONAL No 13700

TODA MODIFICACION AL PROYECTO URBANISTICO DEBE SER AUTORIZADA POR LA DIRECCIÓN DEL PLAN REGULADOR

Obs.

Lam. N°
1
Esc. 1:1200

DIRECCION DE PLAN REGULADOR
GOBIERNO AUTONOMO MUNICIPAL DE COTOCA

APROBADO
PLAN REGULADOR
GOBIERNO AUTONOMO MUNICIPAL DE COTOCA
25 ABR 2023

Arq. Rimberto Méndez Chávez
DIRECTOR PLAN REGULADOR
GOBIERNO AUTONOMO MUNICIPAL DE COTOCA

Fecha: ABRIL 2023